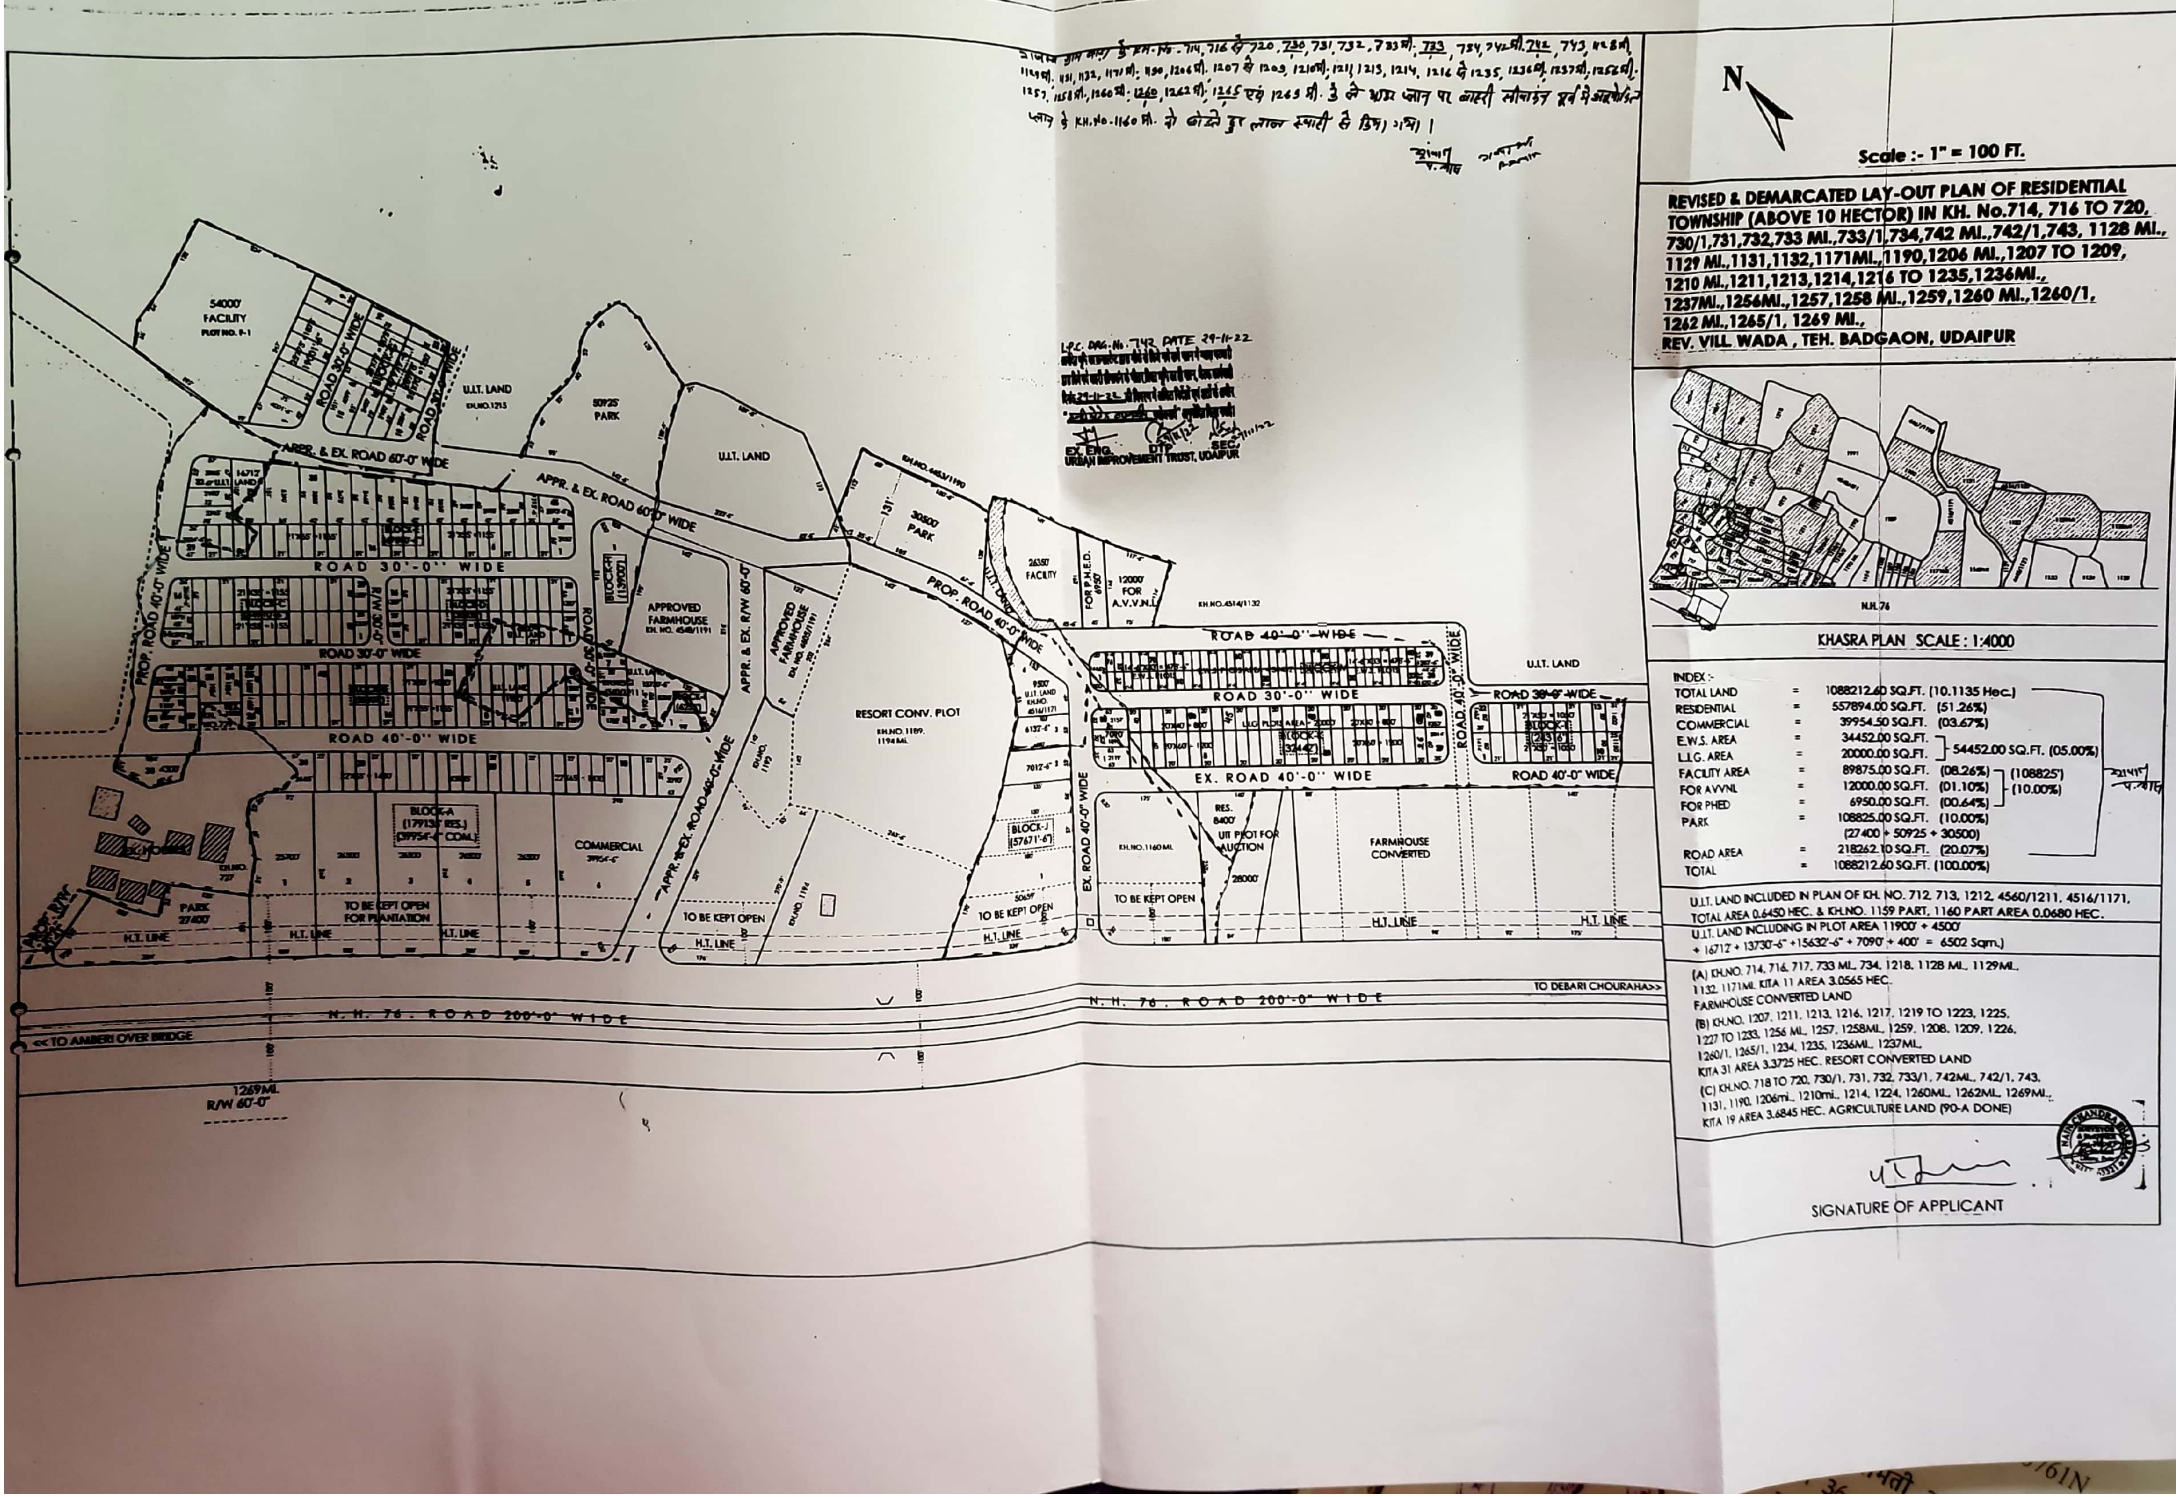

N
Scale :- 1" = 100 FT.
REVISED & DEMARCATED LAY-OUT PLAN OF RESIDENTIAL TOWNSHIP (ABOVE 10 HECTOR) IN KH. No.714, 716 TO 720, 730/1,731,732,733 Mi.,733/1,734,742 Mi.,742/1,743, 1128 Mi., 1129 Mi.,1131,1132,1171Mi.,1190,1206 Mi.,1207 TO 1209, 1210 Mi.,1211,1213,1214,1216 TO 1235,1236Mi., 1237Mi.,1256Mi.,1257,1258 Mi.,1259,1260 Mi.,1260/1, 1262 Mi.,1265/1, 1269 Mi.,
REV. VILL WADA , TEH. BADGAON, UDAIPUR
N.H.76
KHASRA PLAN SCALE : 1:4000
INDEX :-
TOTAL LAND = 1088212.60 SQ.FT. (10.1135 Hec.)
RESIDENTIAL = 557894.00 SQ.FT. (51.26%)
COMMERCIAL = 39954.50 SQ.FT. (03.67%)
E.W.S. AREA = 34452.00 SQ.FT.
L.I.G. AREA = 20000.00 SQ.FT. } 54452.00 SQ.FT. (05.00%)
FACILITY AREA = 89875.00 SQ.FT. (08.26%)
FOR AVVNL = 12000.00 SQ.FT. (01.10%) } (108825') (10.00%)
FOR PHED = 6950.00 SQ.FT. (00.64%)
PARK = 108825.00 SQ.FT. (10.00%)
(27400 + 50925 + 30500)
ROAD AREA = 218262.10 SQ.FT. (20.07%)
TOTAL = 1088212.60 SQ.FT. (100.00%)
U.I.T. LAND INCLUDED IN PLAN OF KH. NO. 712, 713, 1212, 4560/1211, 4516/1171, TOTAL AREA 0.6450 HEC. & KH.NO. 1159 PART, 1160 PART AREA 0.0680 HEC.
U.I.T. LAND INCLUDING IN PLOT AREA 11900' + 4500' + 16712' + 13730'-6" +15632'-6" + 7090' + 400' = 6502 Sqm.)
(A) KH.NO. 714, 716, 717, 733 Mi., 734, 1218, 1128 Mi., 1129Mi., 1132, 1171Mi. KITA 11 AREA 3.0565 HEC.
FARMHOUSE CONVERTED LAND
(B) KH.NO. 1207, 1211, 1213, 1216, 1217, 1219 TO 1223, 1225, 1227 TO 1233, 1256 Mi., 1257, 1258Mi., 1259, 1208, 1209, 1226, 1260/1, 1265/1, 1234, 1235, 1236Mi., 1237Mi.,
KITA 31 AREA 3.3725 HEC. RESORT CONVERTED LAND
(C) KH.NO. 718 TO 720, 730/1, 731, 732, 733/1, 742Mi., 742/1, 743, 1131, 1190, 1206Mi., 1210Mi., 1214, 1224, 1260Mi., 1262Mi., 1269Mi.,
KITA 19 AREA 3.6845 HEC. AGRICULTURE LAND (90-A DONE)
SIGNATURE OF APPLICANT
L.P.C. DAS. No. 742 DATE 29-11-22
EX. ENG. DY. SEC.
URBAN IMPROVEMENT TRUST, UDAIPUR
54000' FACILITY PLOT NO. P-1
U.I.T. LAND KH.NO.1215
50925' PARK
U.I.T. LAND
APPR. & EX. ROAD 60'-0" WIDE
ROAD 30'-0" WIDE
PROP. ROAD 40'-0" WIDE
APPROVED FARMHOUSE EX. NO. 4560/1211
APPROVED FARMHOUSE EX. NO. 4560/1211
RESORT CONV. PLOT KH.NO. 1189, 1194 Mi.
30600' PARK
26350' FACILITY
FOR P.H.E.D.
12000' FOR A.V.V.N.L.
KH.NO. 4514/1132
ROAD 40'-0" WIDE
ROAD 30'-0" WIDE
ROAD 30'-0" WIDE
U.I.T. LAND
EX. ROAD 40'-0" WIDE
ROAD 40'-0" WIDE
BLOCK-A (17713' RES.) (39954'-6" COM.)
COMMERCIAL 39954'-6"
PARK 27400'
TO BE KEPT OPEN FOR PLANTATION
TO BE KEPT OPEN
TO BE KEPT OPEN
BLOCK-J (57671'-6")
RES. 8400' UIT PLOT FOR AUCTION
KH.NO. 1160 Mi.
TO BE KEPT OPEN
FARMHOUSE CONVERTED
H.T. LINE
N. H. 76 . ROAD 200'-0" WIDE
<< TO AMBERI OVER BRIDGE
TO DEBARI CHOURAHA >>
1269Mi. R/W 60'-0"